


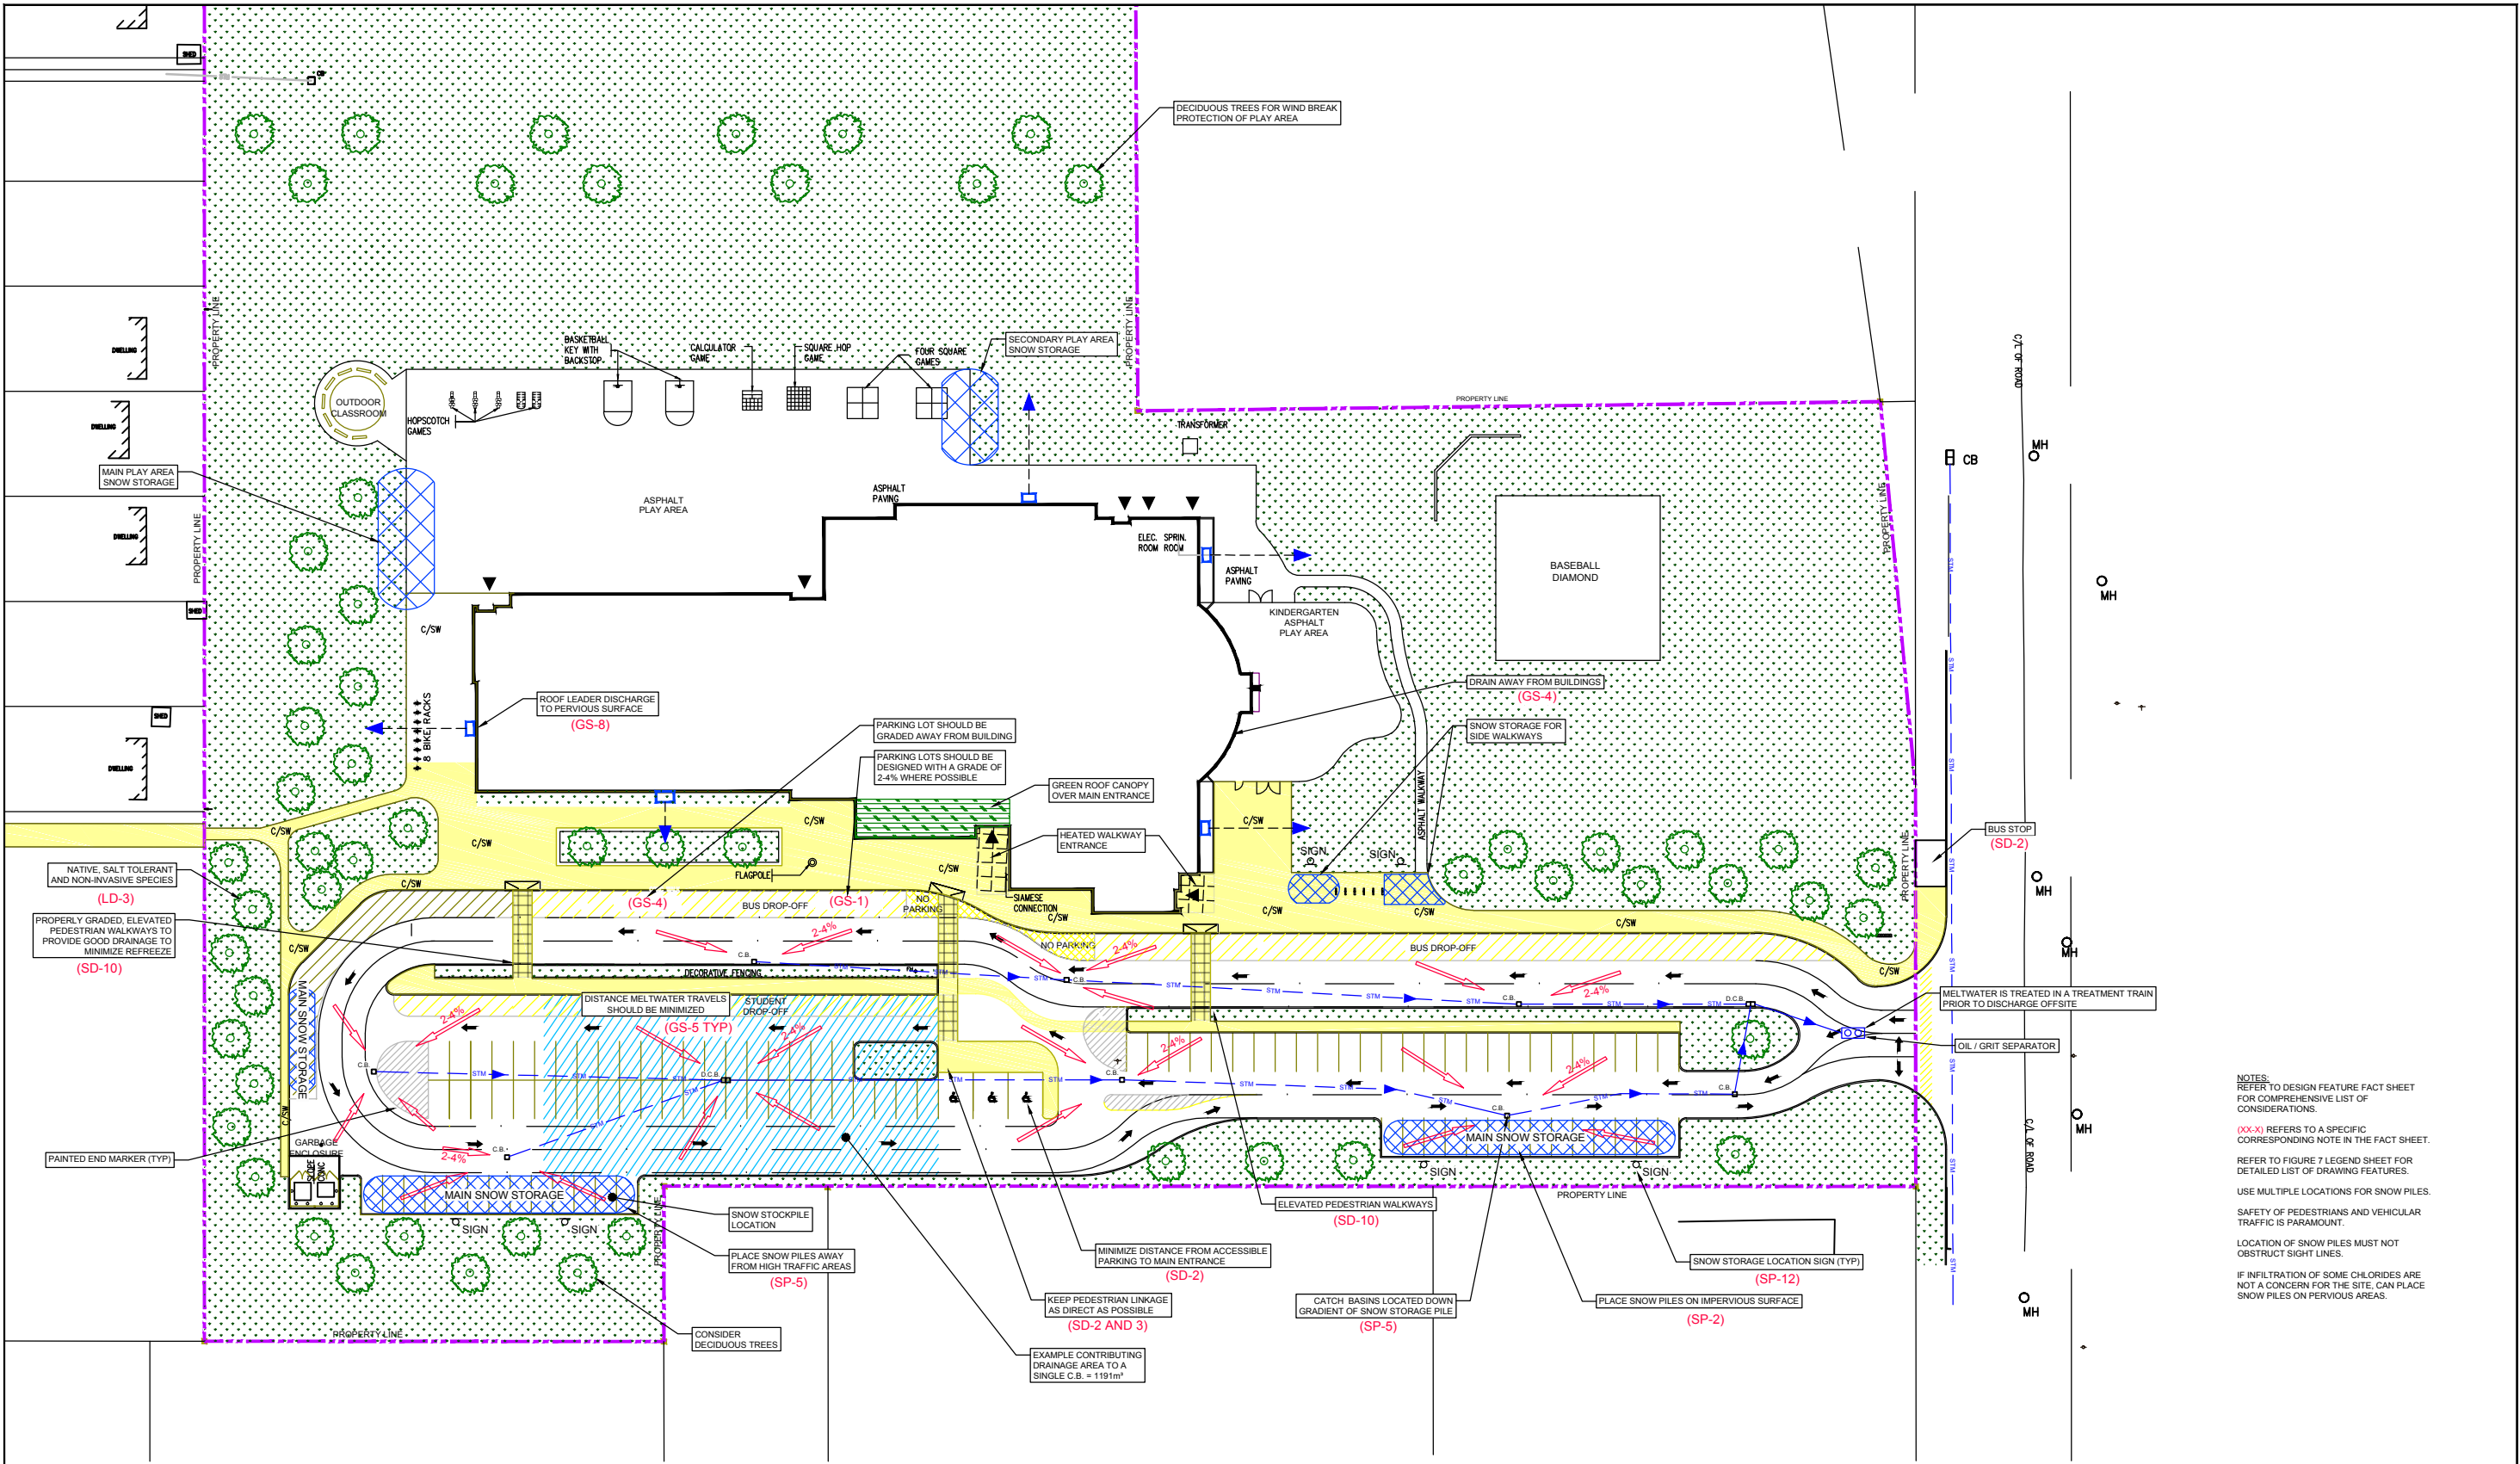

NOTES:
REFER TO DESIGN FEATURE FACT SHEET FOR COMPREHENSIVE LIST OF CONSIDERATIONS.
(XX-X) REFERS TO A SPECIFIC CORRESPONDING NOTE IN THE FACT SHEET.
REFER TO FIGURE 7 LEGEND SHEET FOR DETAILED LIST OF DRAWING FEATURES.
USE MULTIPLE LOCATIONS FOR SNOW PILES.
SAFETY OF PEDESTRIANS AND VEHICULAR TRAFFIC IS PARAMOUNT.
LOCATION OF SNOW PILES MUST NOT OBSTRUCT SIGHT LINES.
IF INFILTRATION OF SOME CHLORIDES ARE NOT A CONCERN FOR THE SITE, CAN PLACE SNOW PILES ON PERVIOUS AREAS.

	</
--	--	----